



LIGHTING PLAN, MAIN FLOOR

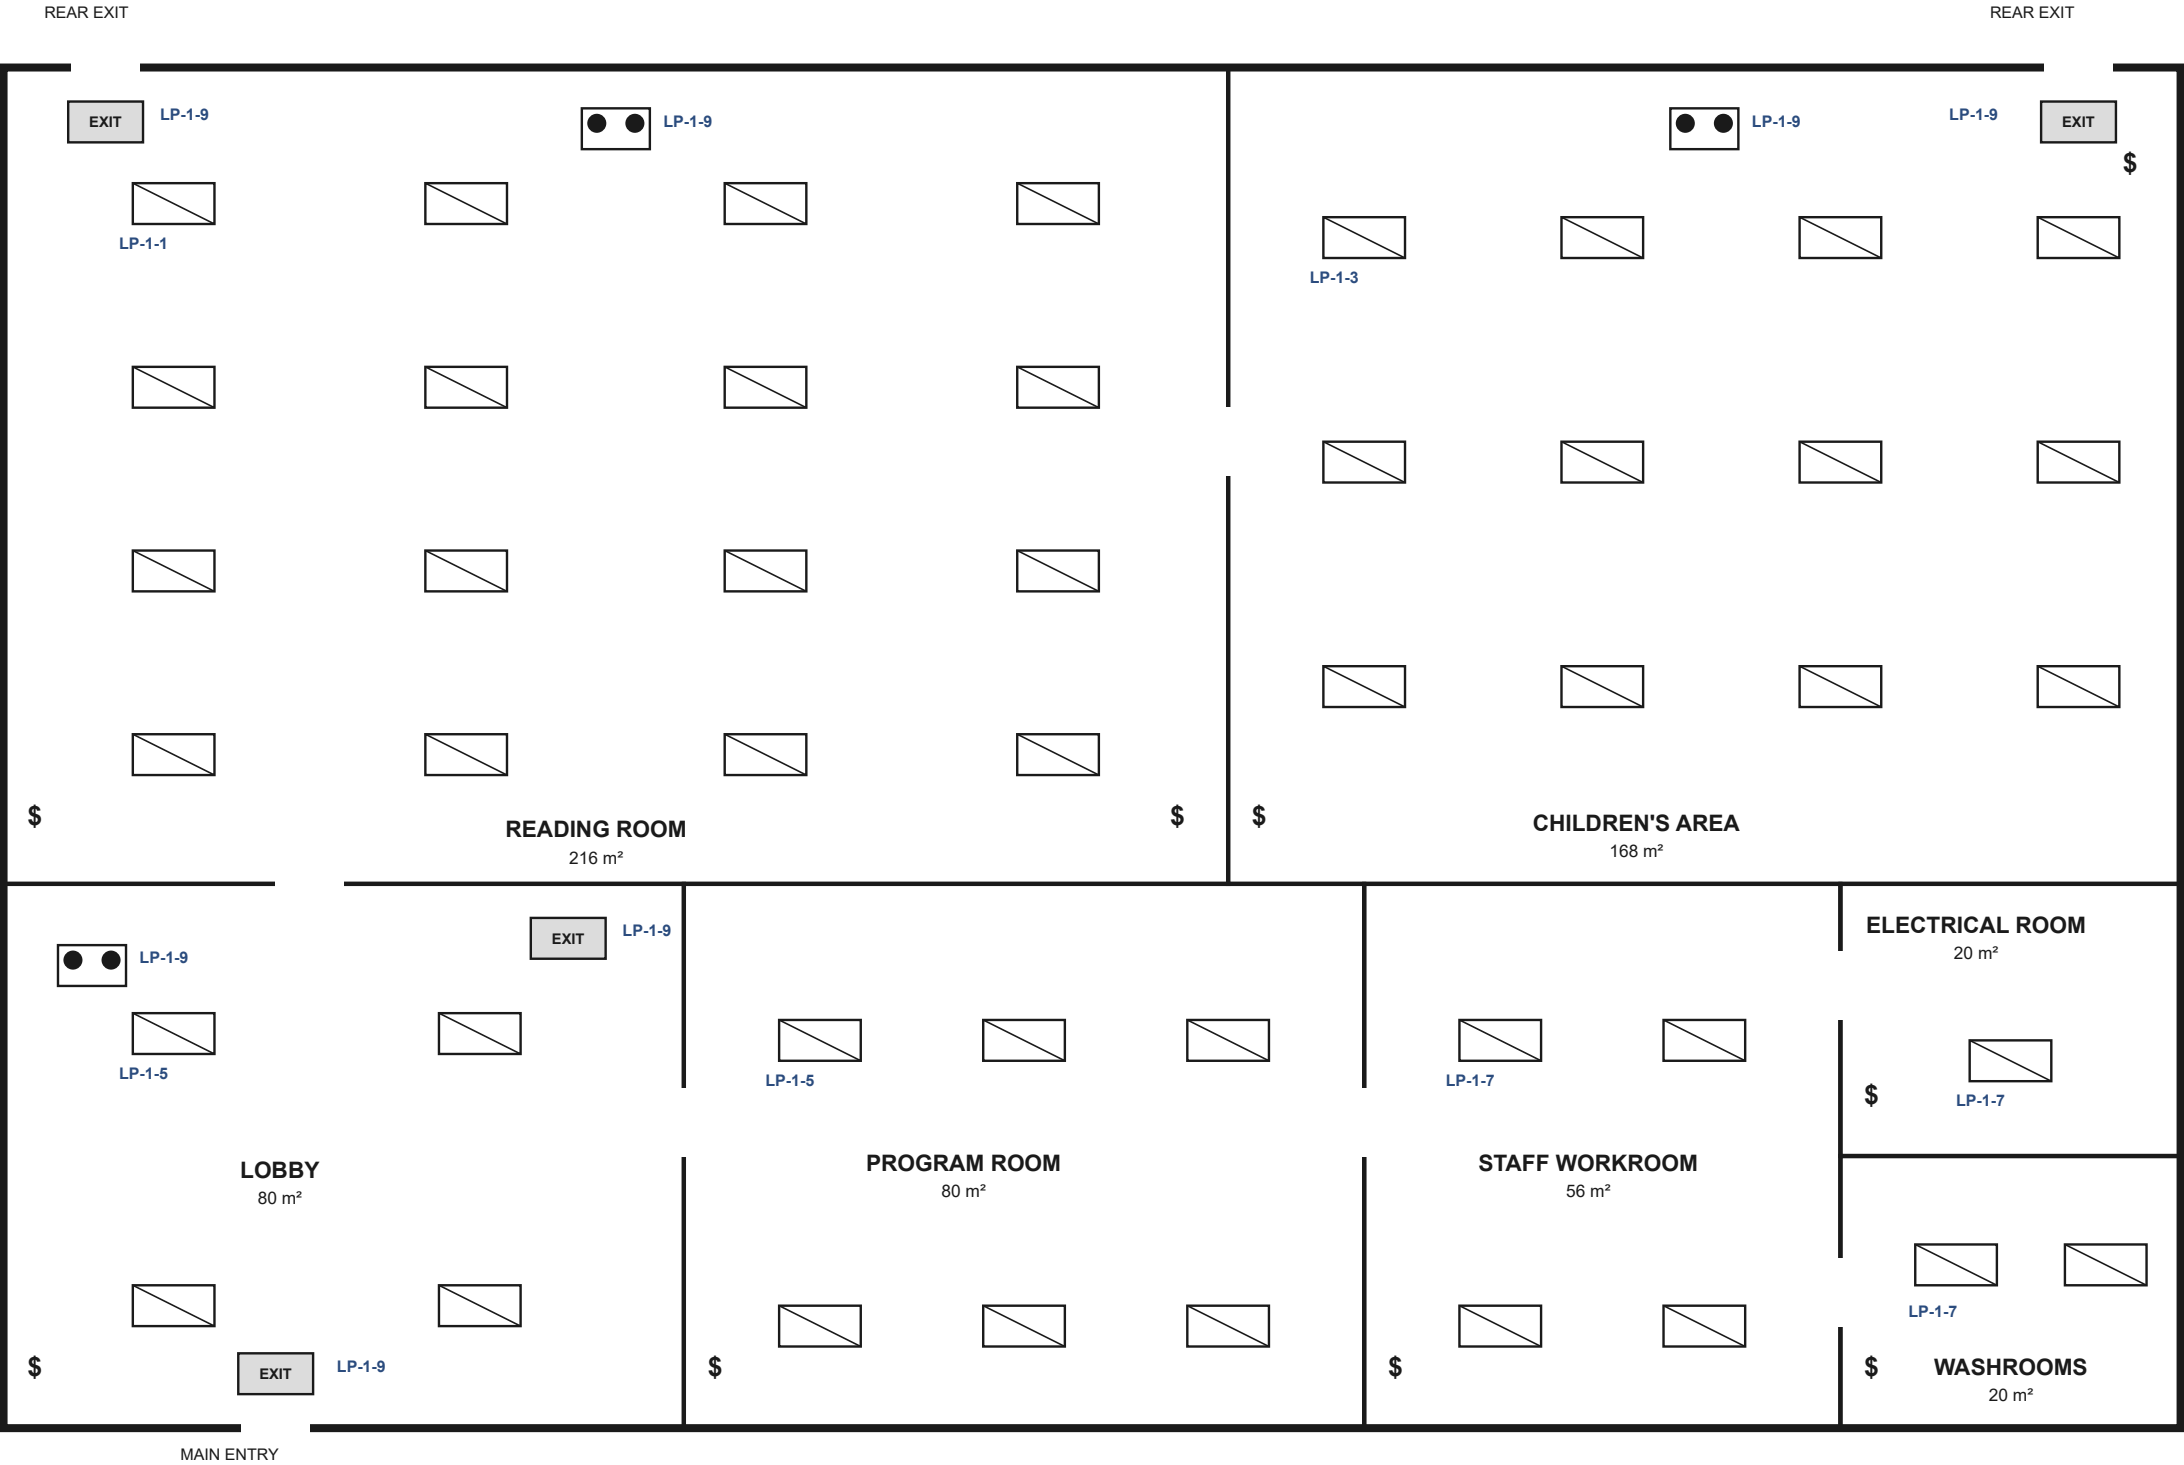

- SHEET NOTES**
- 1. Fixture types and descriptions are on the materials schedule, sheet E-000.
 - 2. Circuit tags name the panel and circuit, for example LP-1-1. All lighting circuits are on panel LP-1, sheet E-002.
 - 3. Exit signs and emergency battery units are on circuit LP-1-9, ahead of any local switch.
 - 4. Switches control the lighting of the room they are in.

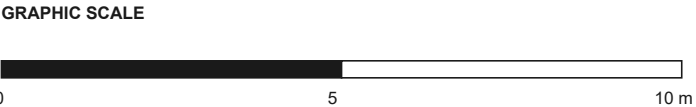

Brightline Consulting Engineers Ltd.
Electrical engineering. Project BCE-26-114

PROJECT
**Quillbrook Public Library, Main Floor
Electrical Fit-out**
2150 Heron Crescent, Quillbrook, Alberta

OWNER
Quillbrook Public Library Board

REVISIONS		
Rev	Description	Date
0	Issued for tender	2026-09-08

SCALE
Graphic scale shown

SHEET TITLE
Lighting Plan, Main Floor

SHEET
E-101