


SINGLE-LINE DIAGRAM

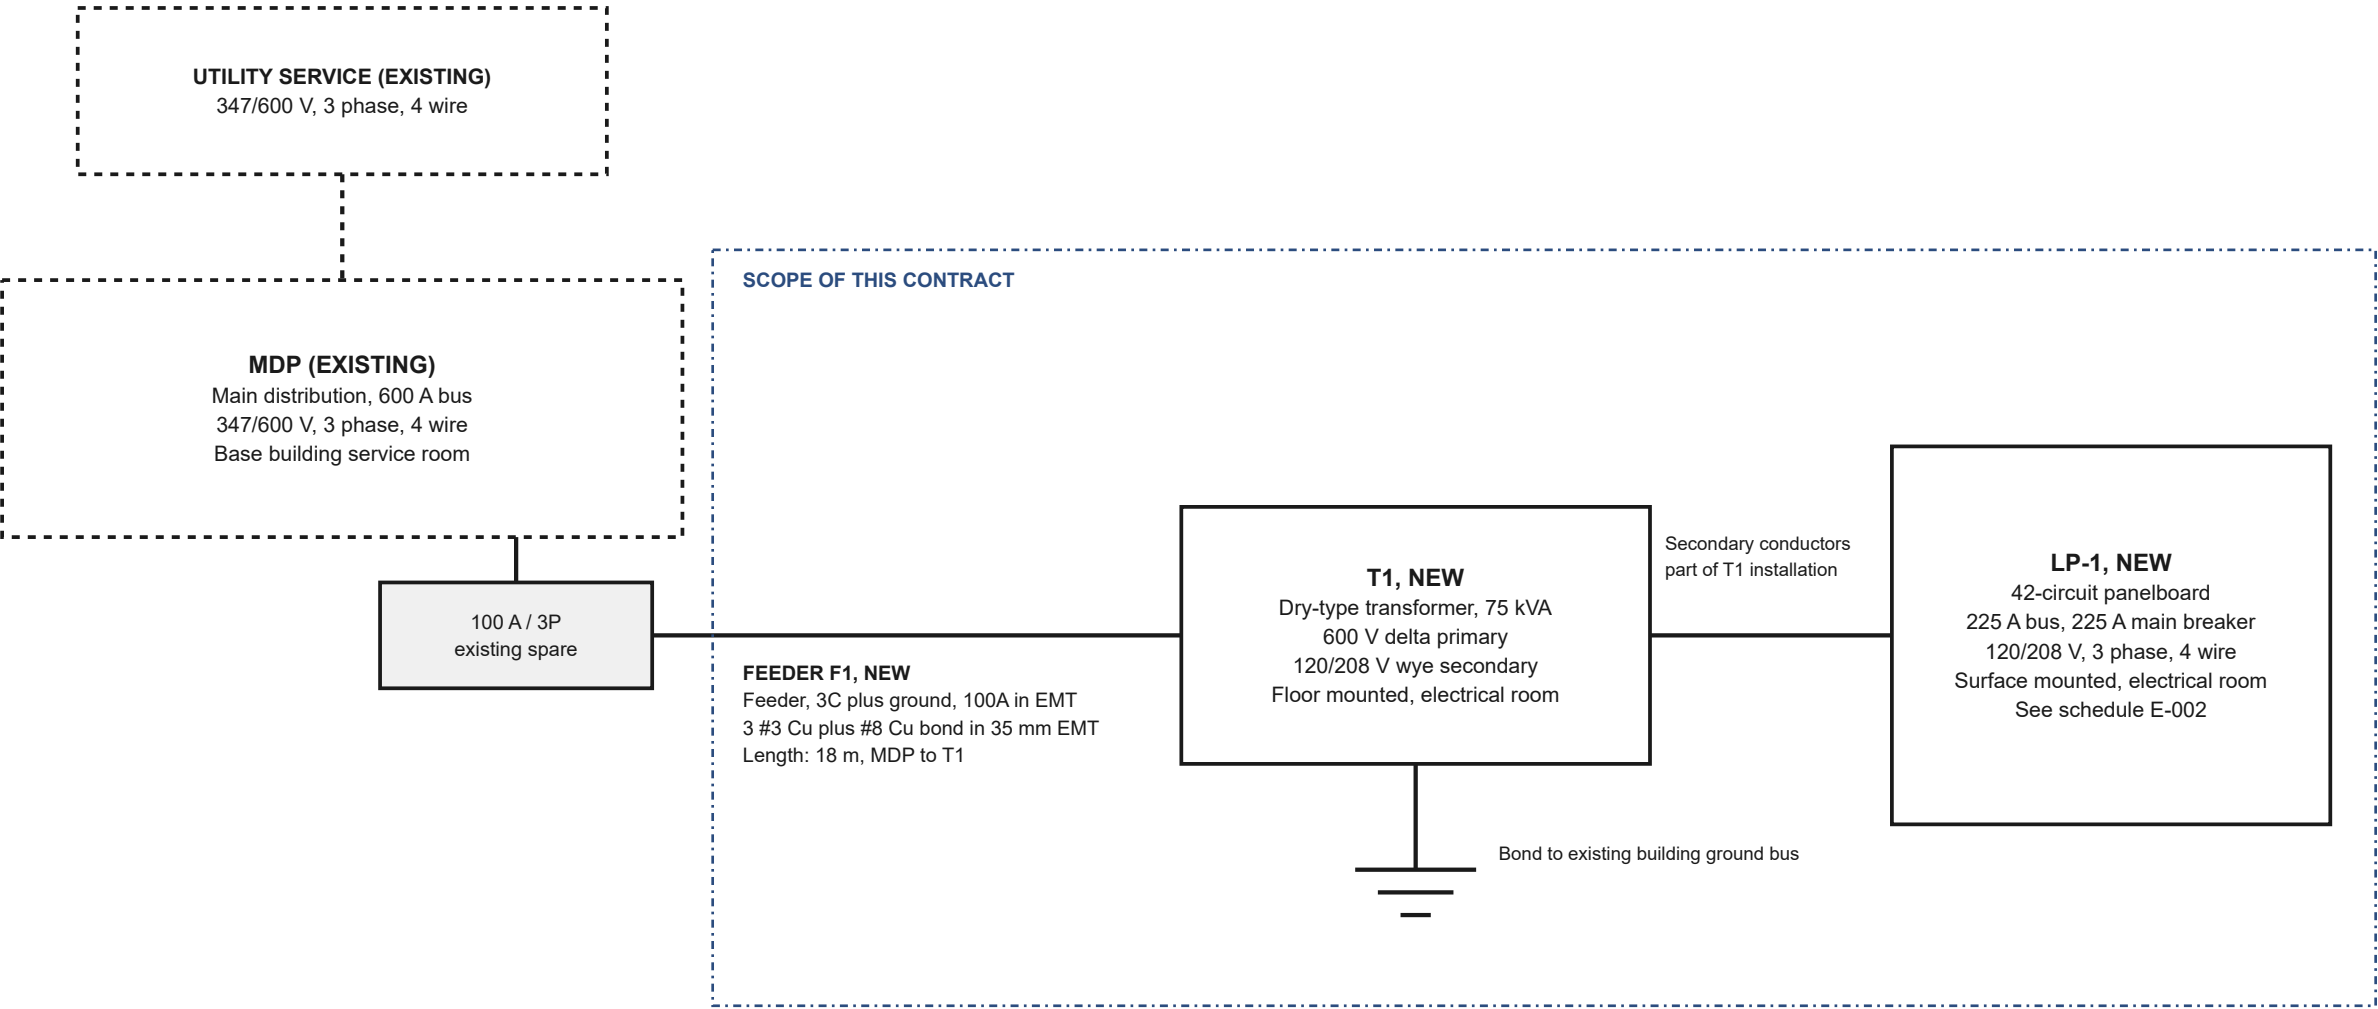

NOTES

- Existing equipment is shown dashed and is not part of this contract, except the connection of feeder F1 to the existing spare 100 A / 3P breaker in MDP.
- Panel LP-1 is sized for a future second-floor fit-out. The main floor connected load is on sheet E-002.

Brightline Consulting Engineers Ltd.

Electrical engineering. Project BCE-26-114

PROJECT

**Quillbrook Public Library, Main Floor
Electrical Fit-out**

2150 Heron Crescent, Quillbrook, Alberta

OWNER

Quillbrook Public Library Board

REVISIONS

Rev	Description	Date
0	Issued for tender	2026-09-08

SCALE

Not to scale

SHEET TITLE

Single-Line Diagram

SHEET

E-001