



POWER PLAN, MAIN FLOOR

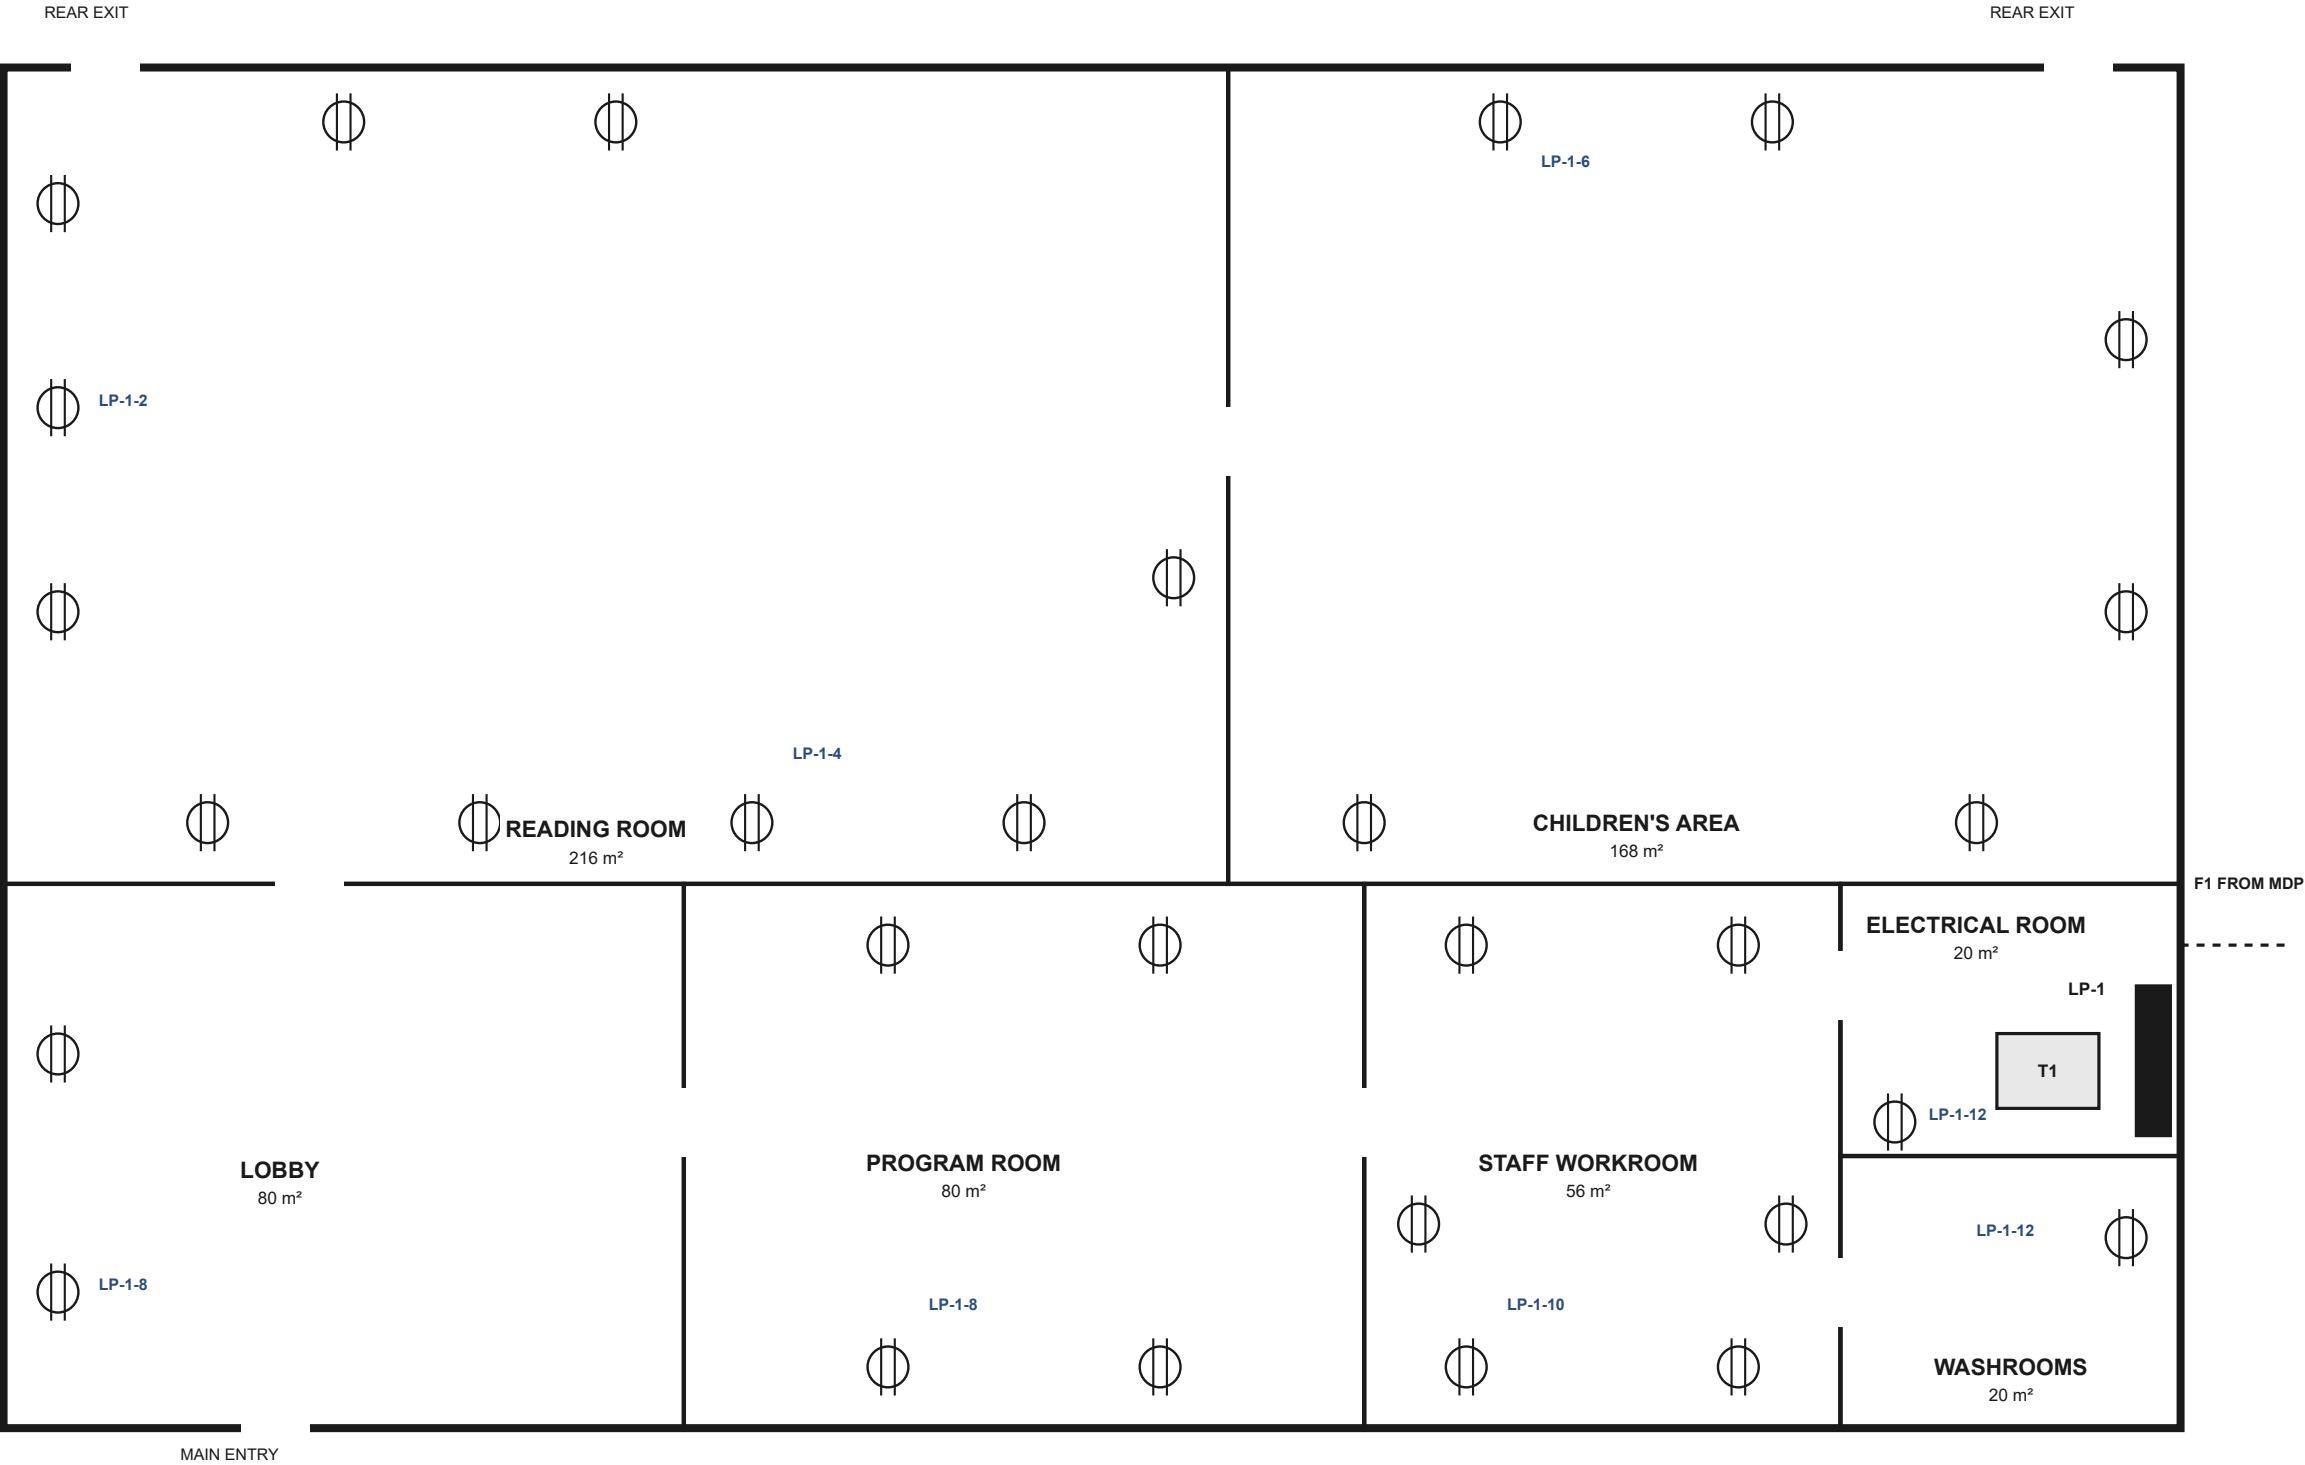

- SHEET NOTES**
- 1. Device descriptions are on the materials schedule, sheet E-000. Receptacles are mounted 400 mm above finished floor unless noted.
 - 2. Circuit tags name the panel and circuit. All receptacle circuits are on panel LP-1, sheet E-002.
 - 3. Transformer T1 and panel LP-1 are in the electrical room. Feeder F1 arrives from the existing main distribution MDP in the base building service room, outside the fit-out area. See single-line diagram E-001.

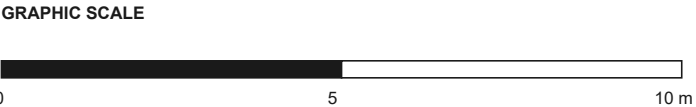

Brightline Consulting Engineers Ltd.
Electrical engineering. Project BCE-26-114

PROJECT
**Quillbrook Public Library, Main Floor
Electrical Fit-out**
2150 Heron Crescent, Quillbrook, Alberta

OWNER
Quillbrook Public Library Board

REVISIONS		
Rev	Description	Date
0	Issued for tender	2026-09-08

SCALE
Graphic scale shown

SHEET TITLE
Power Plan, Main Floor

SHEET
E-102